

LAND SURVEY

PT PMA KAPAN KITA BERSAMA

PACITAN - EAST JAVA

Pantai Watukarung





Project Location

Image © 2020 Maxar Technologies
Image © 2020 CNES / Airbus
Image © 2020 TerraMetrics

DRAWING LIST :

- | | |
|---------------------------------------|---------------|
| 1. GOOGLE EARTH VIEW | NTS |
| 2. DRAWING LIST | NTS |
| 3. OVERALL PLAN & CONTOUR DRAWING | SCALE 1 : 600 |
| 4. SLOPE ARROWS & SLOPE ARROWS TABLE | SCALE 1 : 600 |
| 5. WATER DROP ANALYSIS | SCALE 1 : 600 |
| 6. ELEVATIONS COLOR SCHEMES | SCALE 1 : 600 |
| 7. SECTION DRAWING A-A; B-B; C-C | SCALE 1 : 600 |
| 8. SECTION DRAWING 1-1; 2-2; 3-3; 4-4 | SCALE 1 : 500 |

PAPER SIZE A3

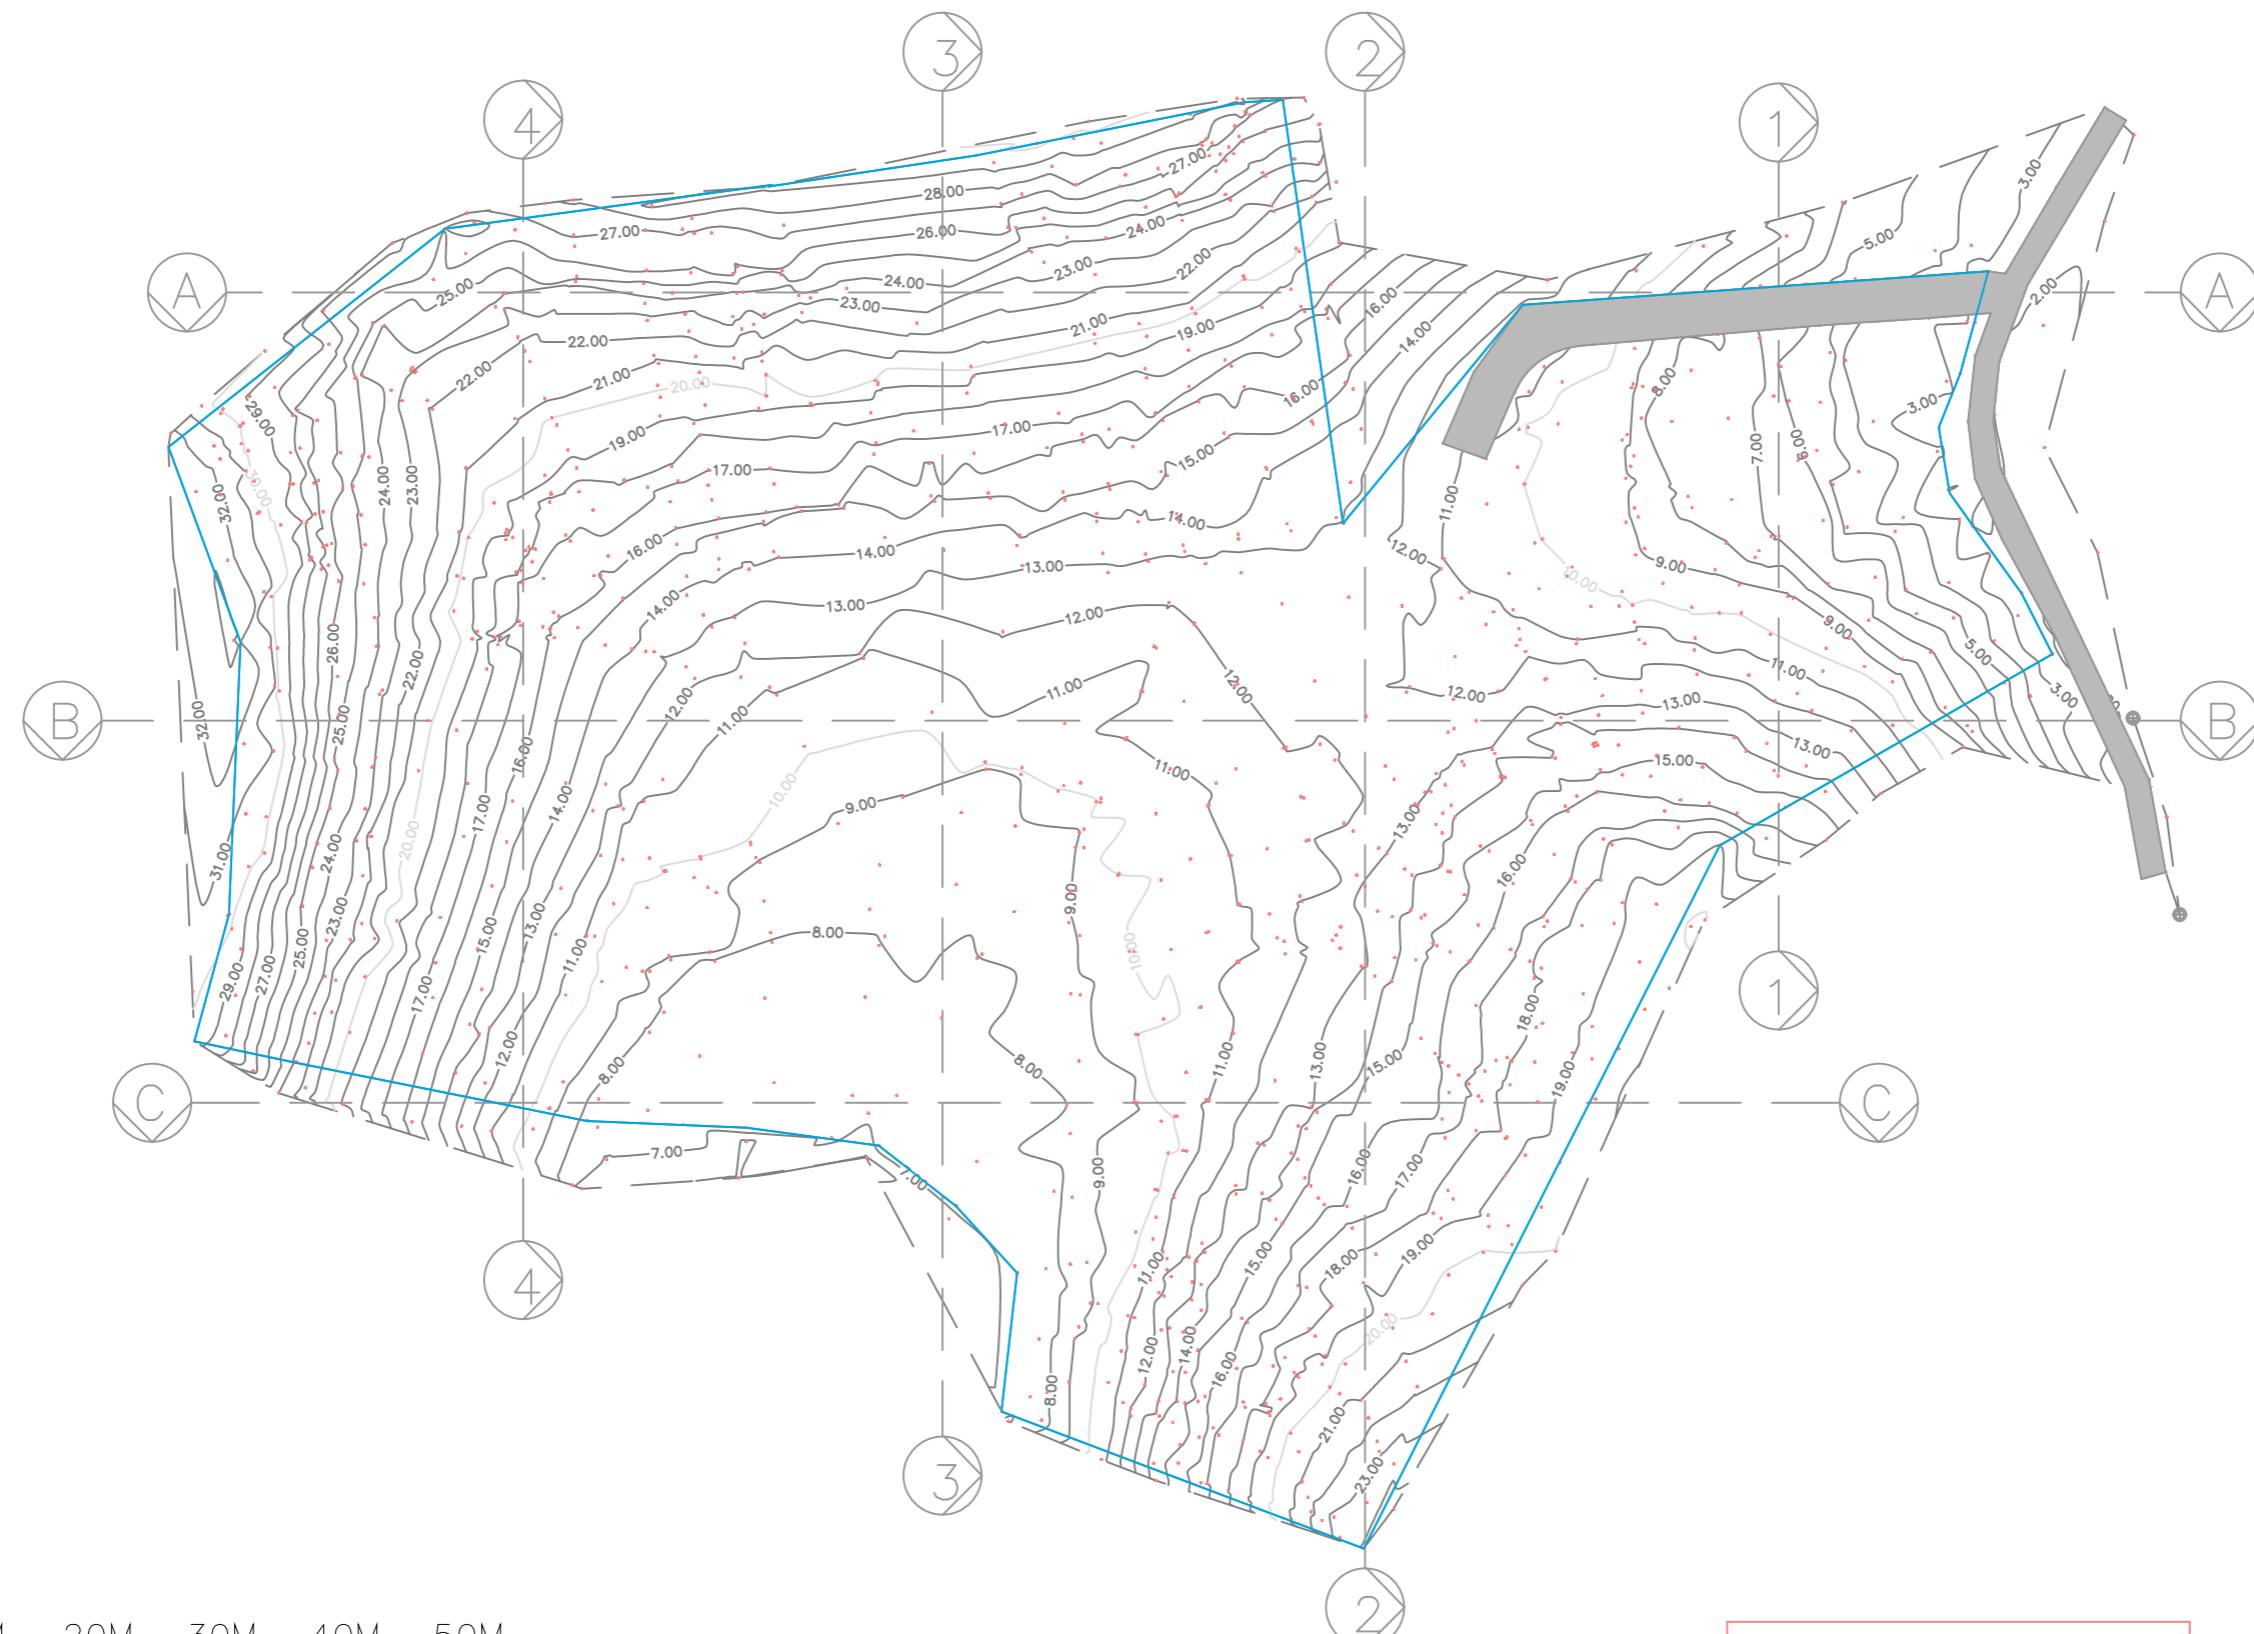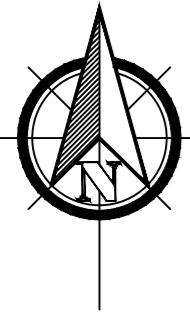

esp

EDI SUPRIYANTO & PARTNERS
Multidisciplinary Engineering Consultant
Bali - Indonesia
Email : edisupriyanto@gmail.com

- LANDSURVEY
- SOIL INVESTIGATION
- STRUCTURAL ENGINEERING

GENERAL NOTE

PROJECT :
TOPOGRAPHY SURVEY

CLIENT :
PT PMA KAPAN KITA BERSAMA
WATUKARUNG - PRINGKUKU
PACITAN - EAST JAVA

LEGEND :

CODE	DESCRIPTION
●	Benchmark Nail
—	Land Boundary
---	Surveyed Area
X ⁸³ BP ⁷²	Point Survey
(A)	Section Line
— 10.00	Major Contour Line
— 11.00	Minor Contour Line
→	Slope Arrows
—	Water Drops
■	Pathway

No	Description	Revision	Date	By



SUBMISSION	
FOR INFORMATION	
SURVEYED BY	CHECKED BY
NAUFAL MAJID ST	EDI SUPRIYANTO ST
DATE:	SCALE:
20MAY20	1 : 600
DWG. TITTLE :	

OVERALL PLAN &
CONTOUR DRAWING

DWG. NO.

ESP/SRV/04/V/2020

PAPER SIZE A3

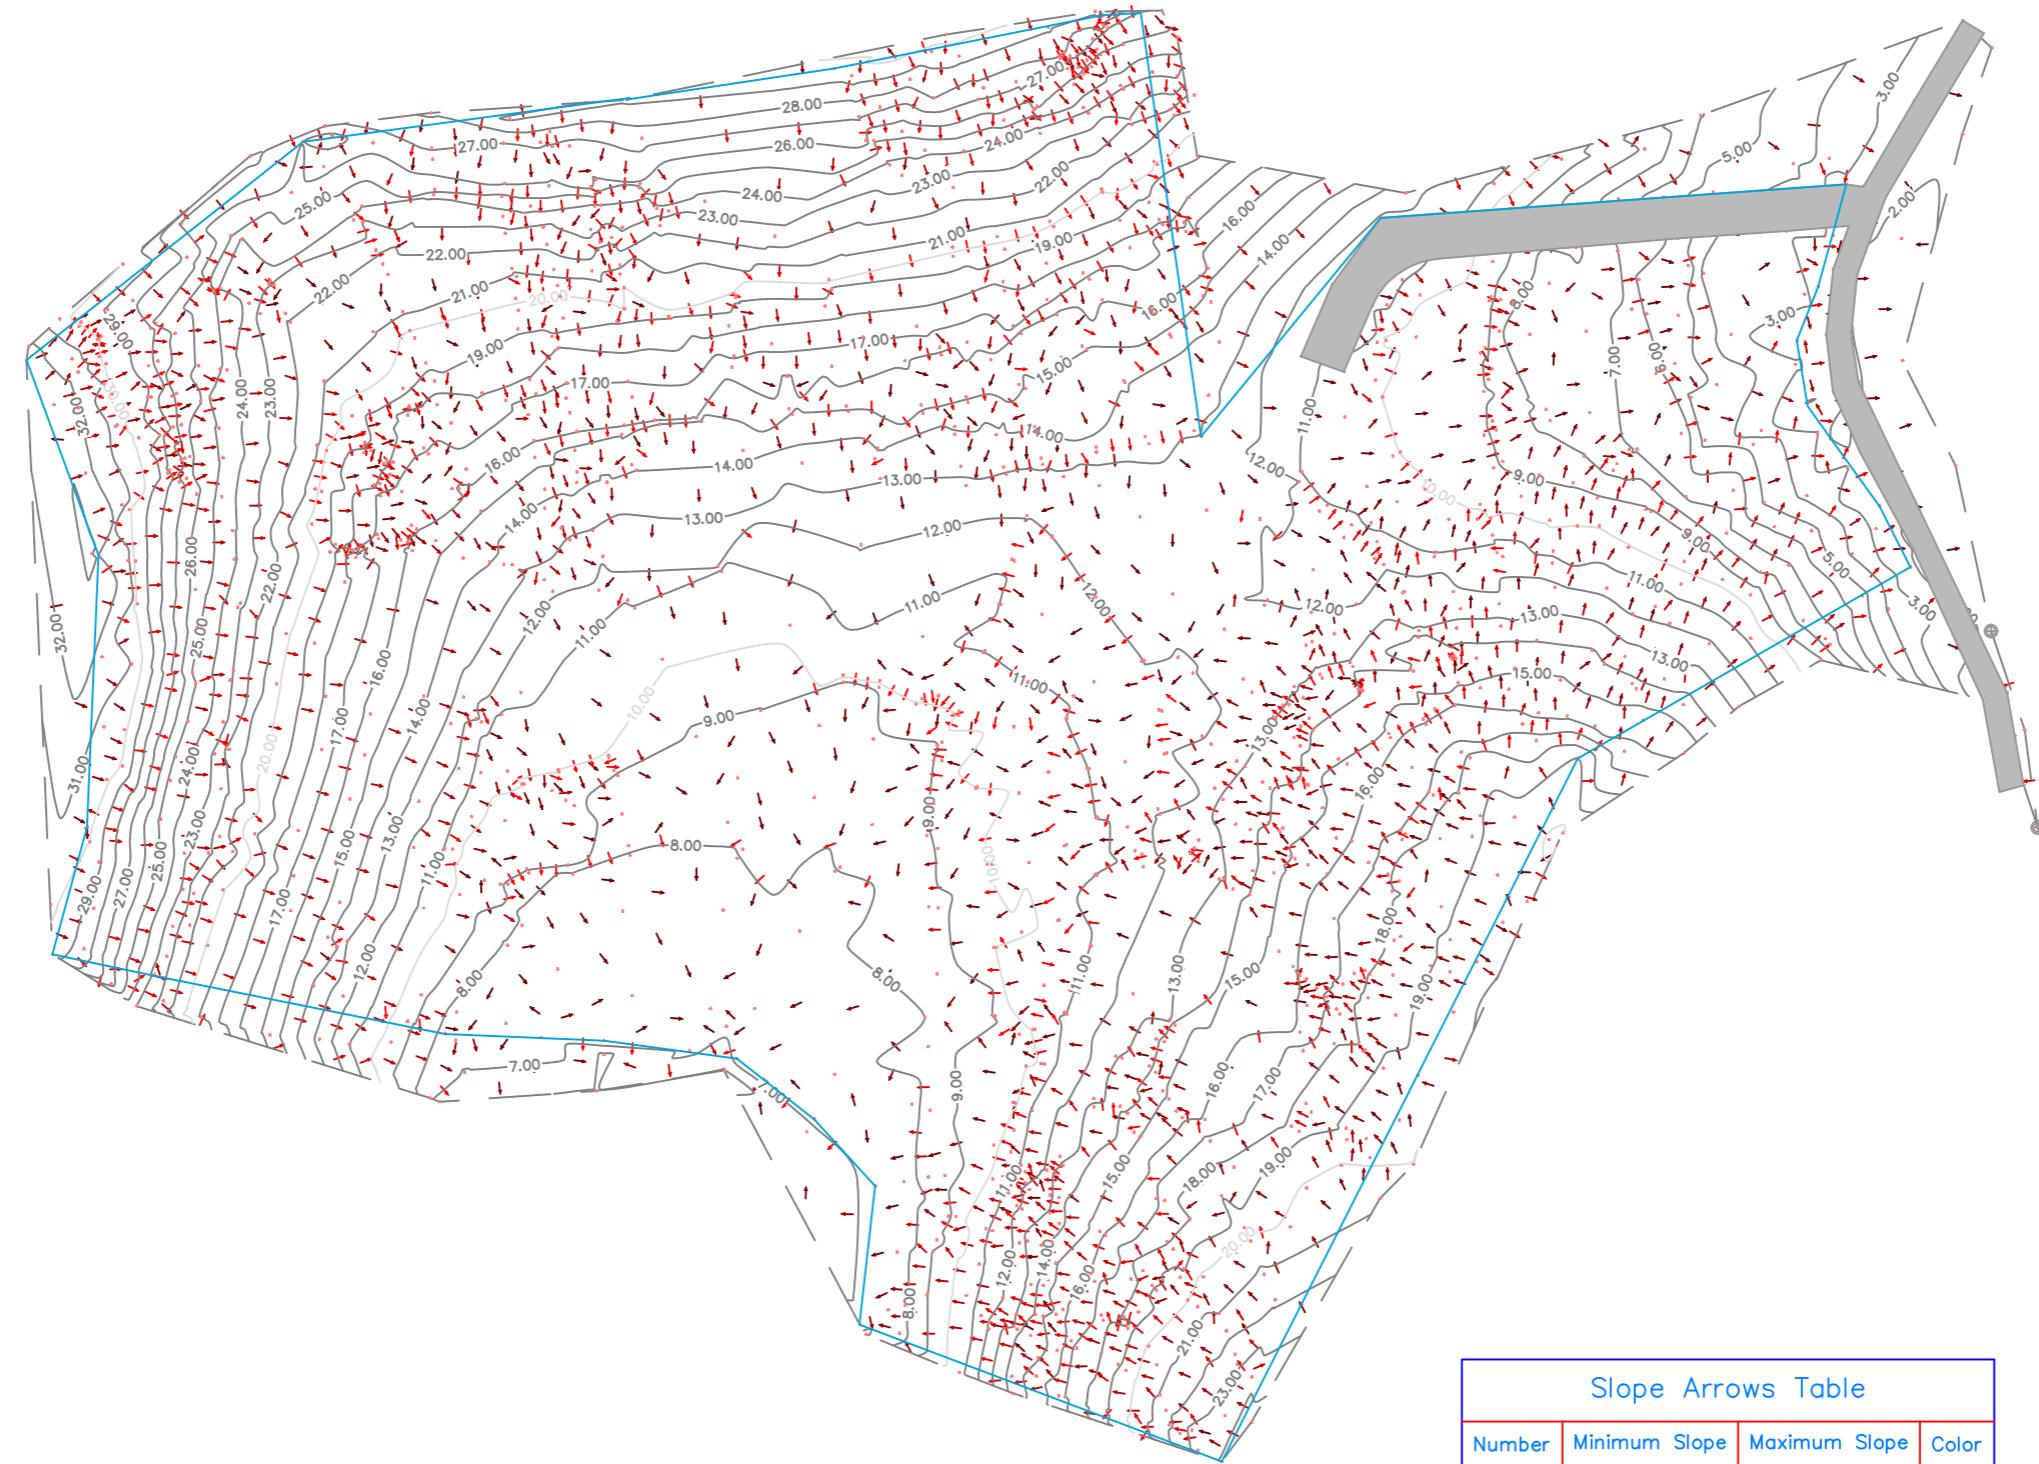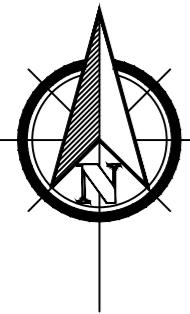


Slope Arrows Table

Number	Minimum Slope	Maximum Slope	Color
1	0.41%	20.61%	Dark Blue
2	20.61%	39.78%	Medium Blue
3	39.78%	60.35%	Red
4	60.35%	104.41%	Dark Red
5	104.41%	8077.88%	Very Dark Red

esp EDI SUPRIYANTO & PARTNERS Multidisciplinary Engineering Consultant Bali - Indonesia Email : edisupriyanto@gmail.com				
- LANDSURVEY - SOIL INVESTIGATION - STRUCTURAL ENGINEERING				
GENERAL NOTE				
PROJECT : TOPOGRAPHY SURVEY				
CLIENT : PT PMA KAPAN KITA BERSAMA WATUKARUNG - PRINGKUKU PACITAN - EAST JAVA				
LEGEND :				
CODE	DESCRIPTION			
●	Benchmark Nail			
—	Land Boundary			
—	Surveyed Area			
X ⁸³ ₇₂ BP	Point Survey			
(A)	Section Line			
—	Major Contour Line			
—	Minor Contour Line			
→	Slope Arrows			
—	Water Drops			
■	Pathway			
No	Description	Revision	Date	By
SUBMISSION				
FOR INFORMATION				
SURVEYED BY <input checked="" type="checkbox"/> CHECKED BY				
NAUFAL MAJID ST <input type="checkbox"/> EDI SUPRIYANTO ST				
DATE: <input type="text"/> SCALE:				
20MAY20 <input type="text"/> 1 : 600				
DWG. TITTLE: <input type="text"/>				
SLOPE ARROWS				
DWG. NO. <input type="text"/>				
ESP/SRV/05/V/2020				

PAPER SIZE A3

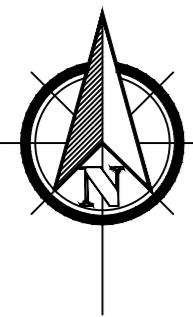

esp

EDI SUPRIYANTO & PARTNERS
Multidisciplinary Engineering Consultant
Bali - Indonesia
Email : edisupriyanto@gmail.com

- LANDSURVEY
- SOIL INVESTIGATION
- STRUCTURAL ENGINEERING

GENERAL NOTE

PROJECT :
TOPOGRAPHY SURVEY

CLIENT :
PT PMA KAPAN KITA BERSAMA
WATUKARUNG - PRINGKUKU
PACITAN - EAST JAVA

LEGEND :

CODE	DESCRIPTION
●	Benchmark Nail
—	Land Boundary
---	Surveyed Area
X ⁸³ BP ⁷²	Point Survey
(A)	Section Line
—	Major Contour Line
—	Minor Contour Line
→	Slope Arrows
—	Water Drops
■	Pathway


No	Description	Revision	Date	By

SUBMISSION	
FOR INFORMATION	
SURVEYED BY	CHECKED BY
NAUFAL MAJID ST	EDI SUPRIYANTO ST
DATE:	SCALE:
20MAY20	1 : 600
DWG. TITTLE :	



WATER DROP ANALYSIS

DWG. NO.

ESP/SRV/06/V/2020

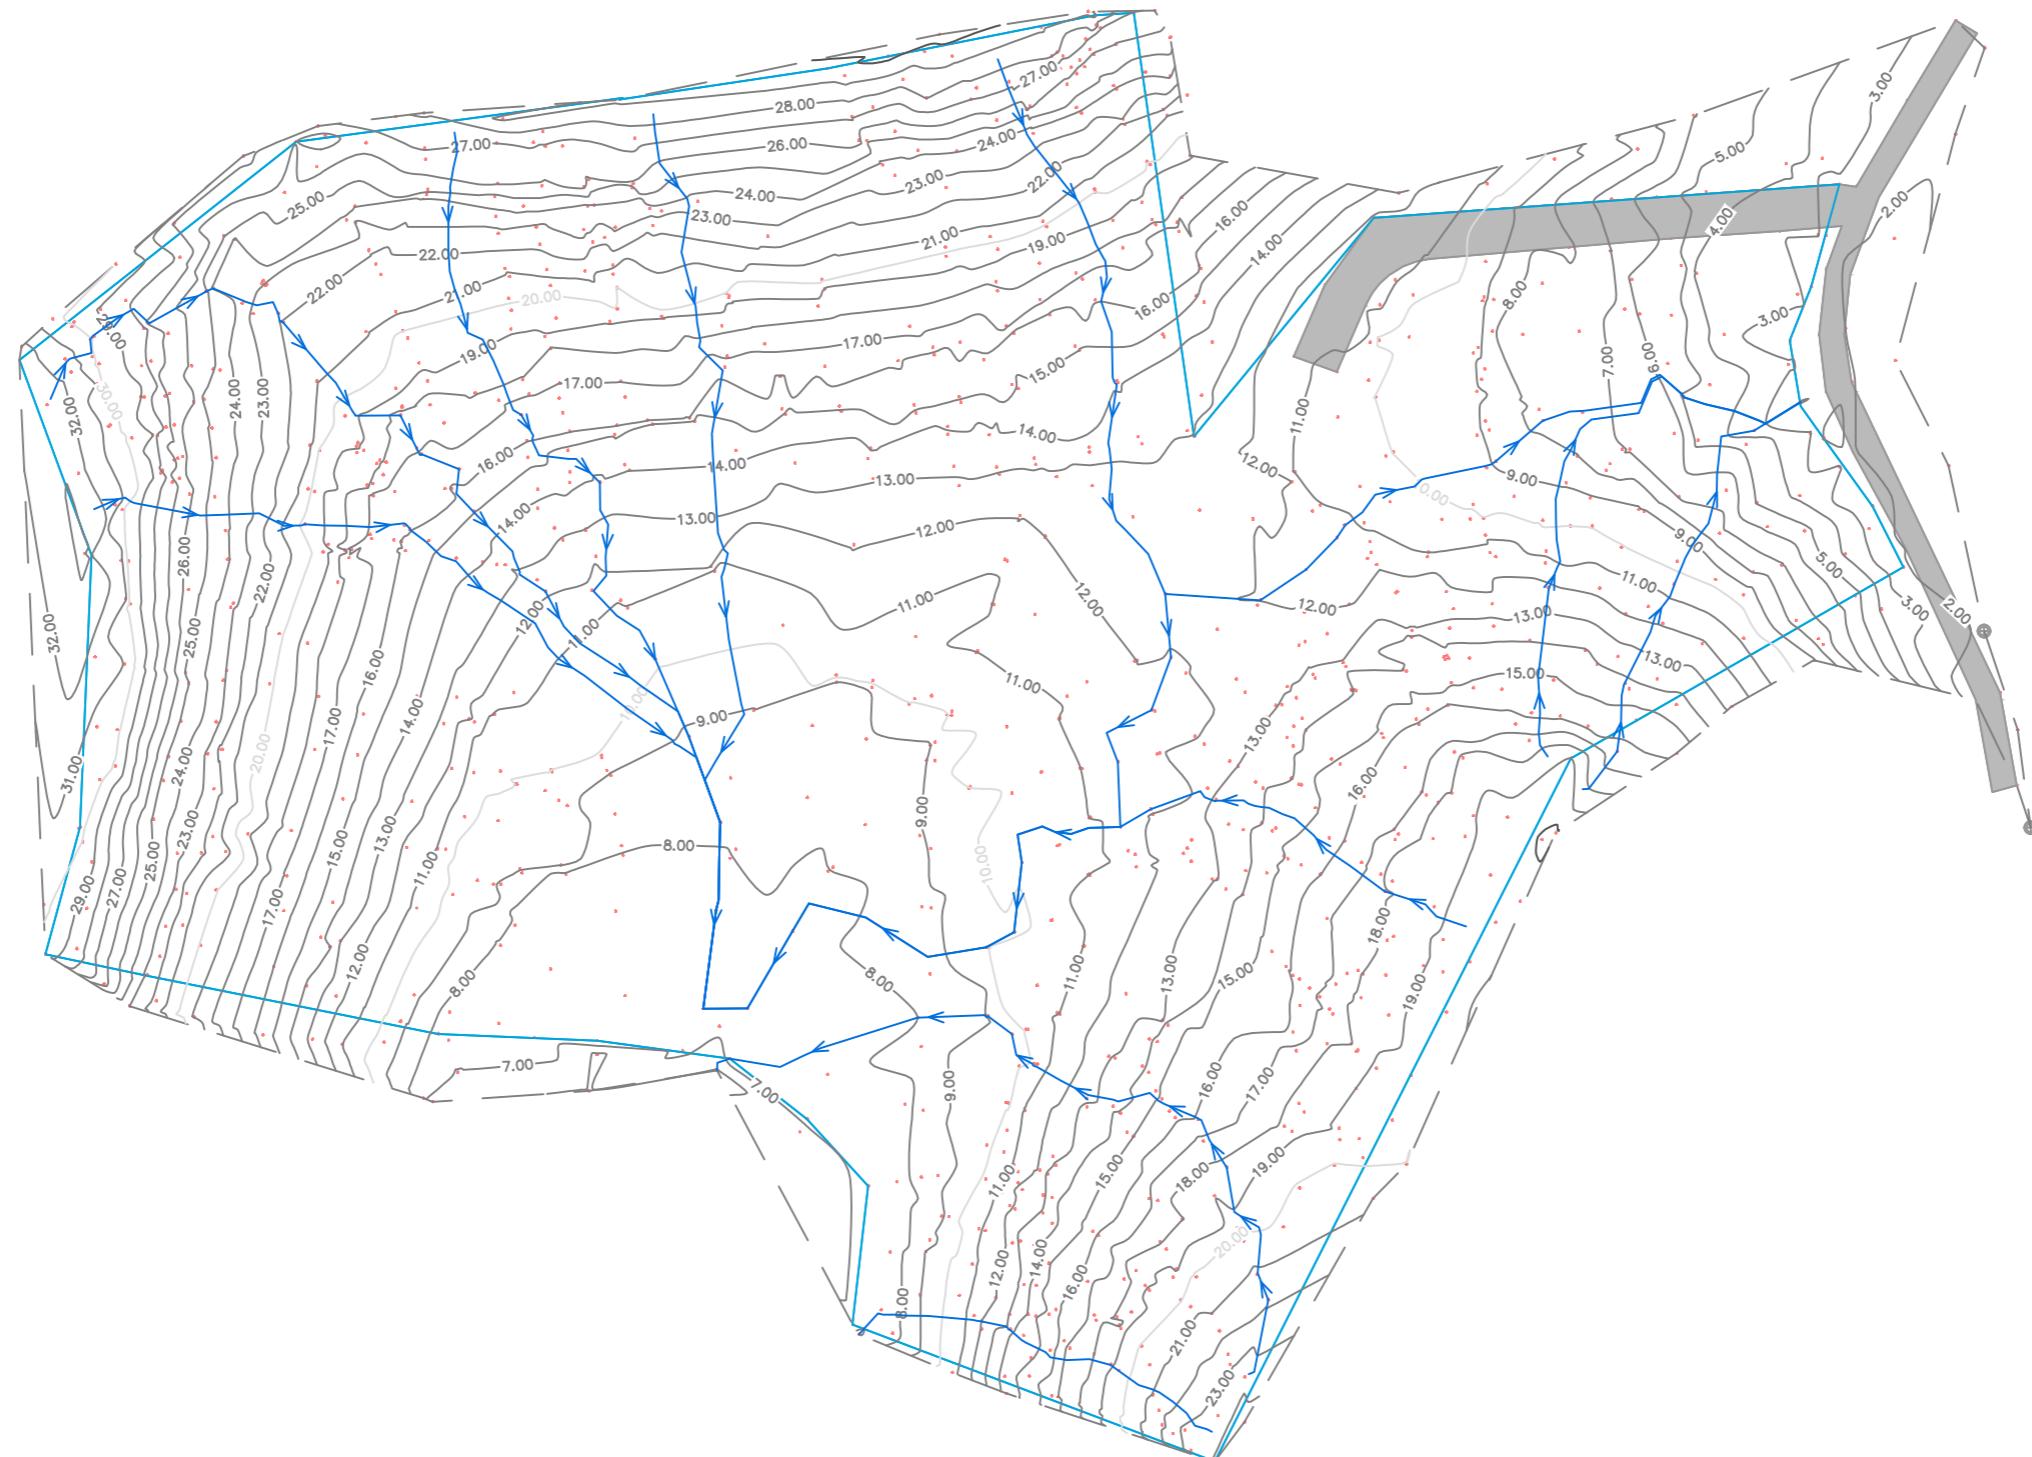


PAPER SIZE A3

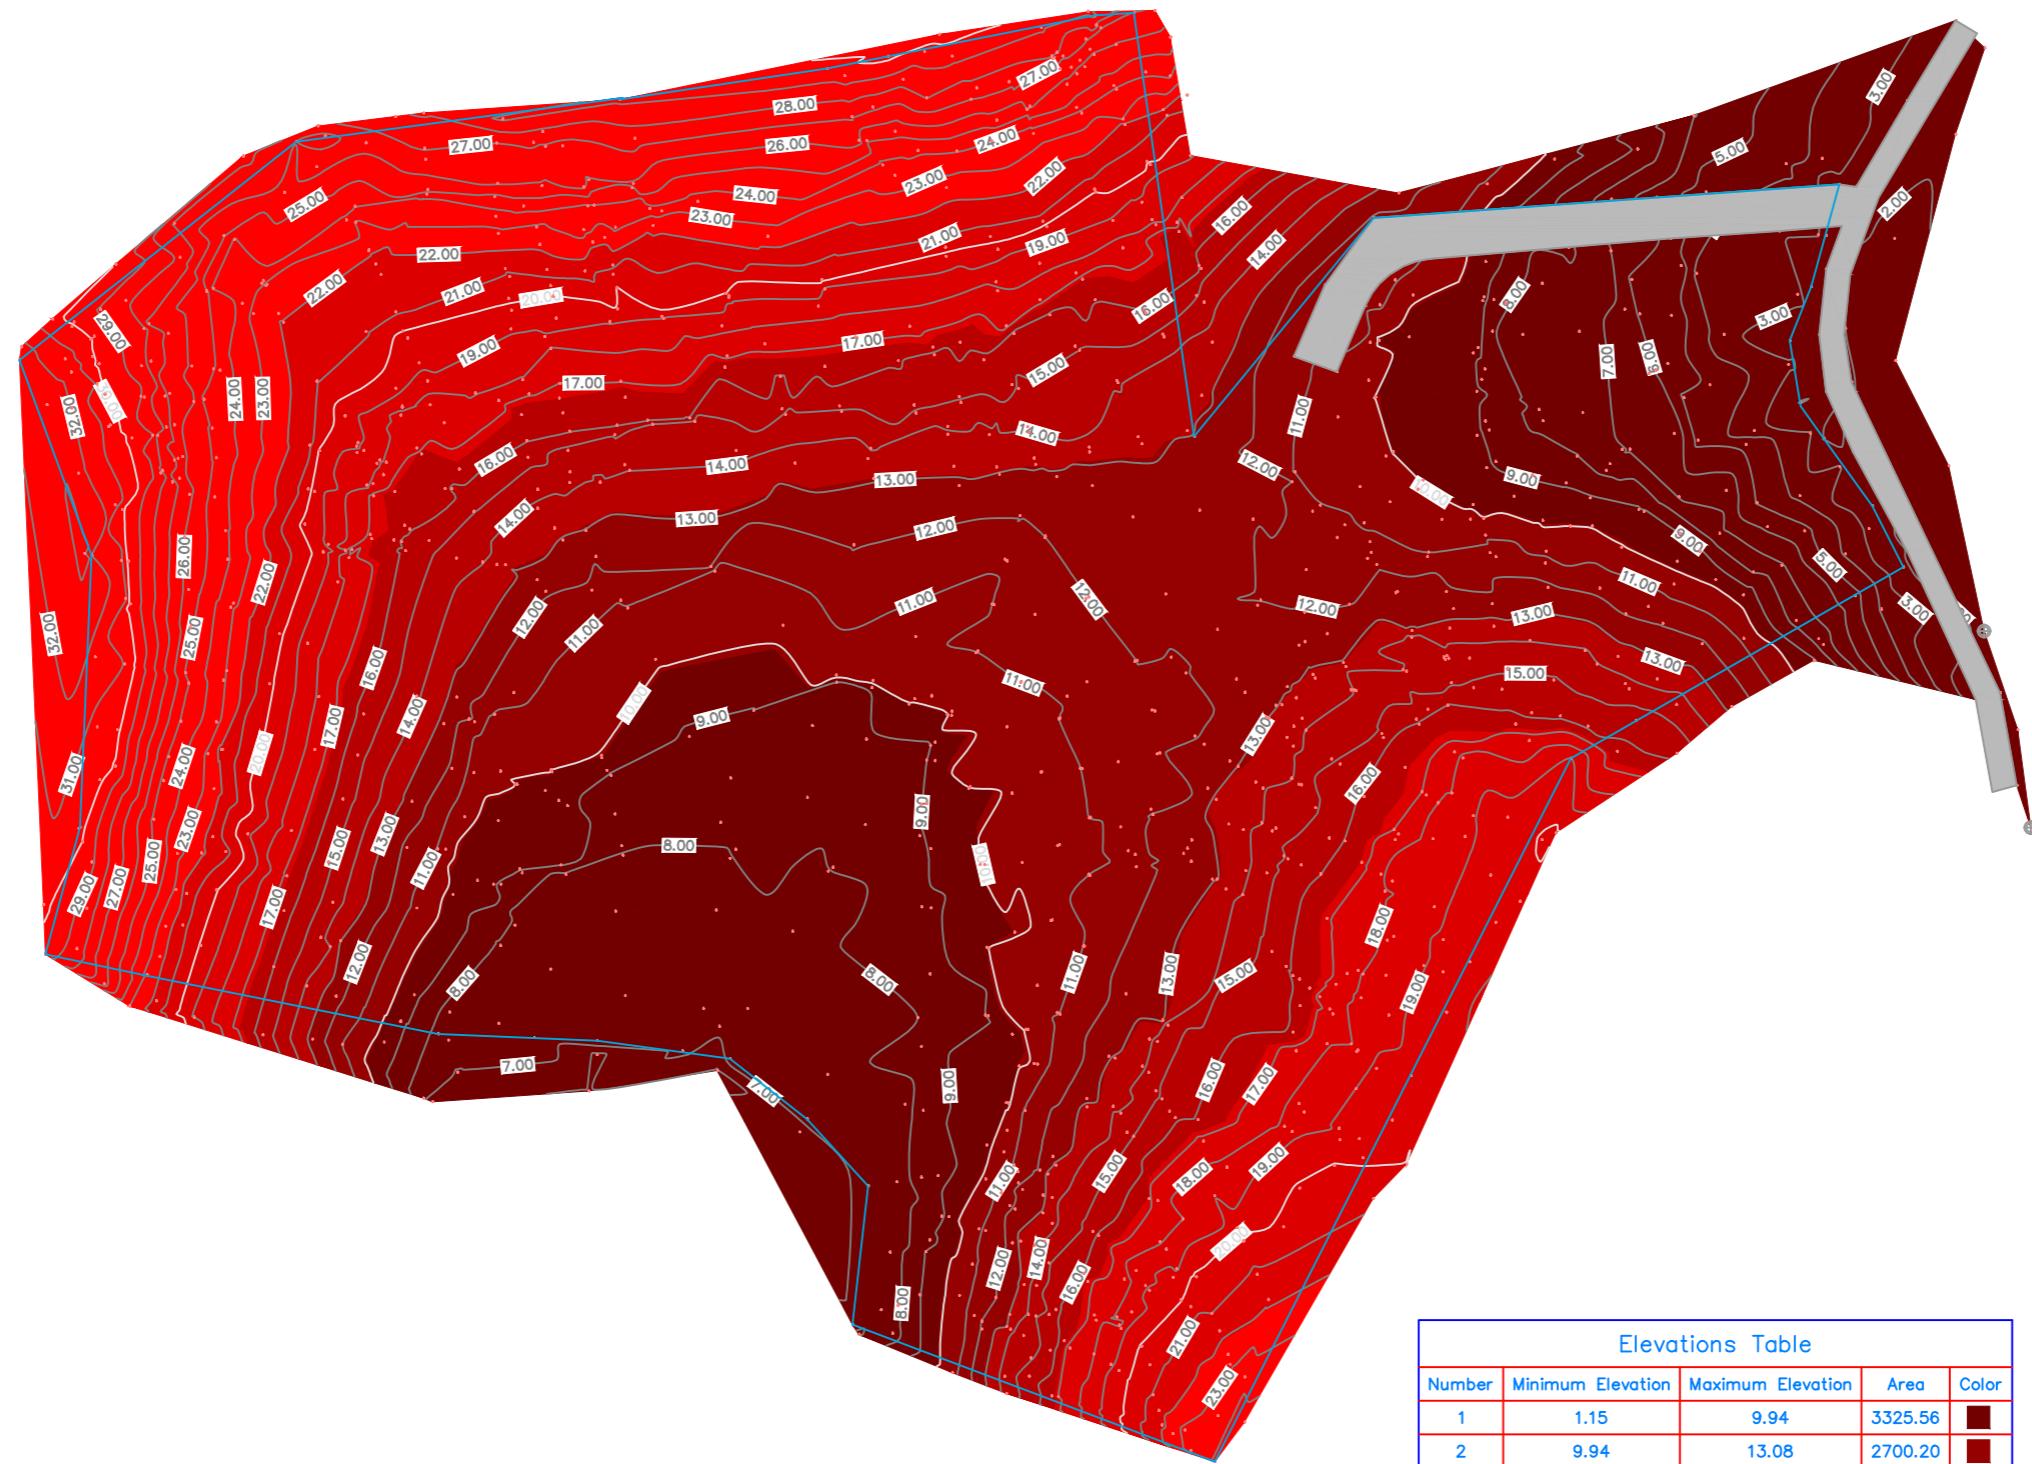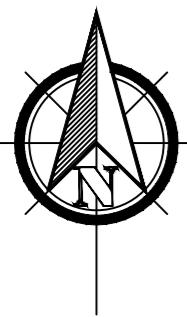

Elevations Table

Number	Minimum Elevation	Maximum Elevation	Area	Color
1	1.15	9.94	3325.56	█
2	9.94	13.08	2700.20	█
3	13.08	16.74	1979.52	█
4	16.74	22.05	2160.43	█
5	22.05	33.23	2007.06	█


PAPER SIZE A3

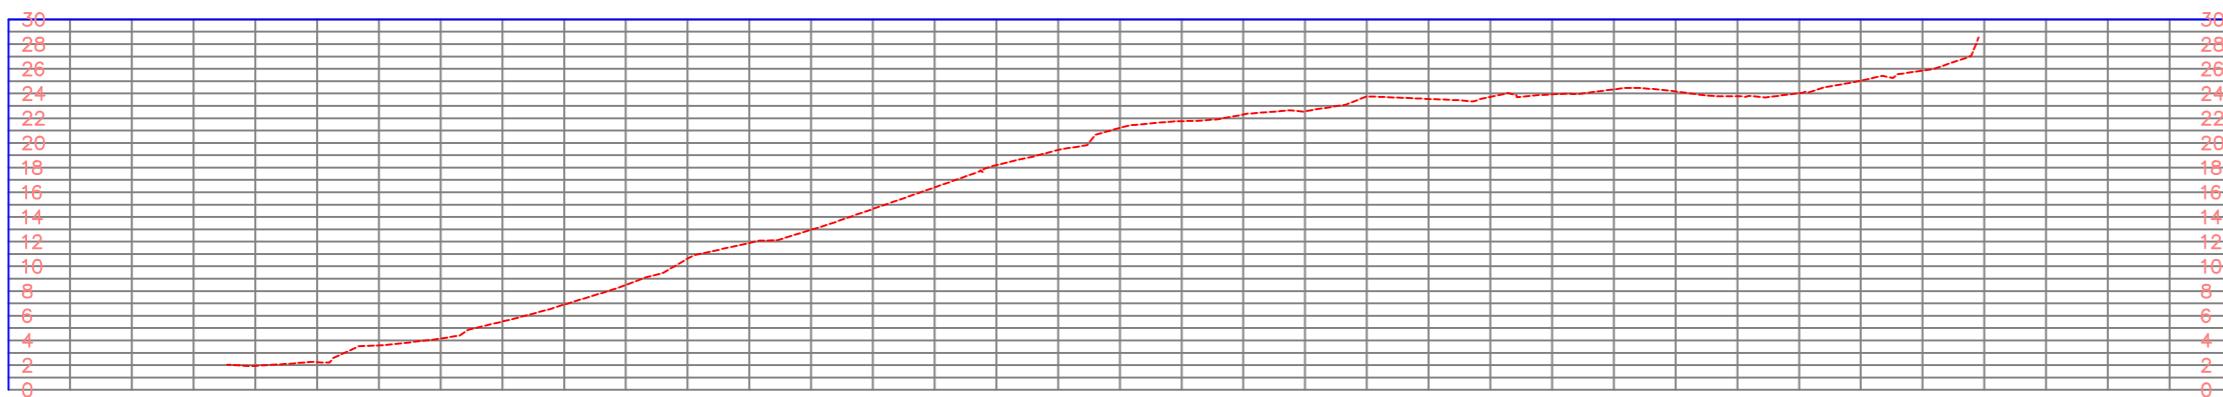


SECTION A - A
SCALE 1 : 600



SECTION B - B

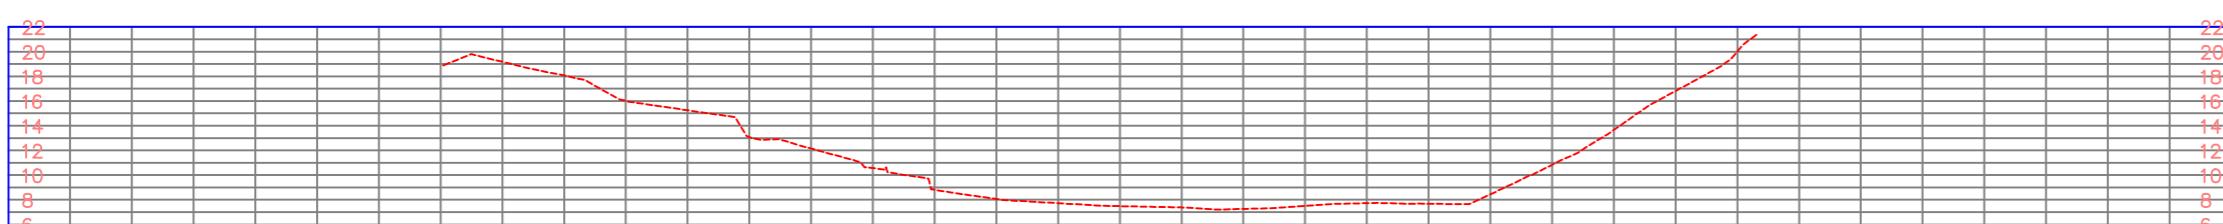

SECTION C - C

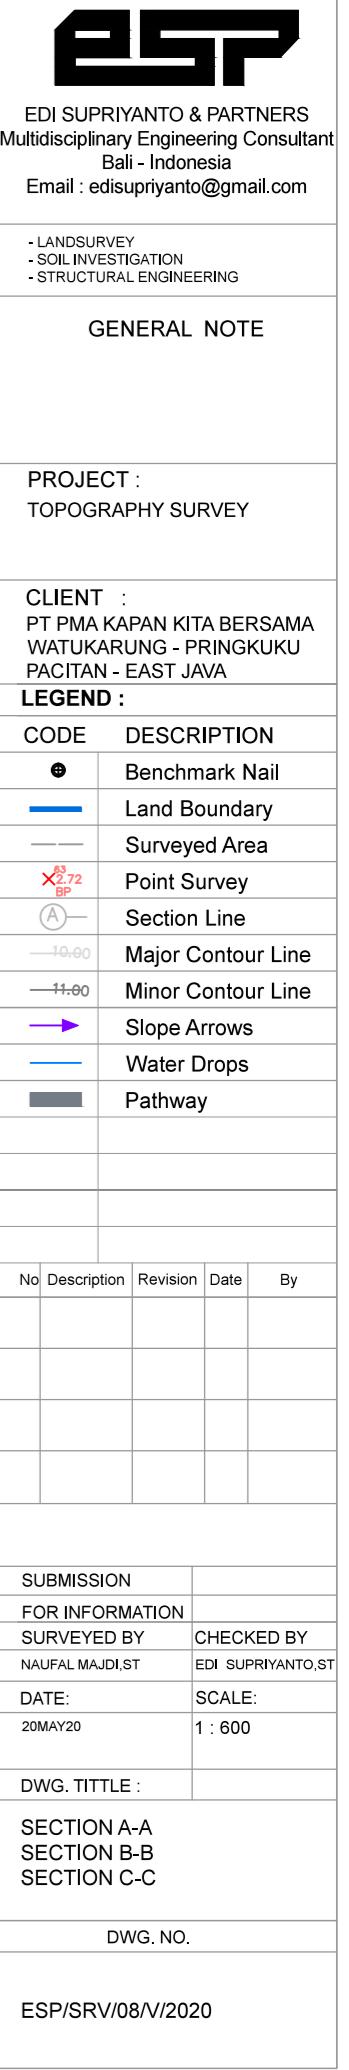

PAPER SIZE A3



EDI SUPRIYANTO & PARTNERS
Multidisciplinary Engineering Consultant
Bali - Indonesia
Email : edisupriyanto@gmail.com

- LANDSURVEY
- SOIL INVESTIGATION
- STRUCTURAL ENGINEERING

GENERAL NOTE


PROJECT :
TOPOGRAPHY SURVEY

CLIENT :
PT PMA KAPAN KITA BERSAMA
WATUKARUNG - PRINGKUKU
PACITAN - EAST JAVA


LEGEND :

CODE	DESCRIPTION
●	Benchmark Nail
—	Land Boundary
---	Surveyed Area
X ⁸³ _{BP} ⁷²	Point Survey
(A) —	Section Line
— 10.00	Major Contour Line
— 11.00	Minor Contour Line
→	Slope Arrows
—	Water Drops
■	Pathway


No	Description	Revision	Date	By
----	-------------	----------	------	----

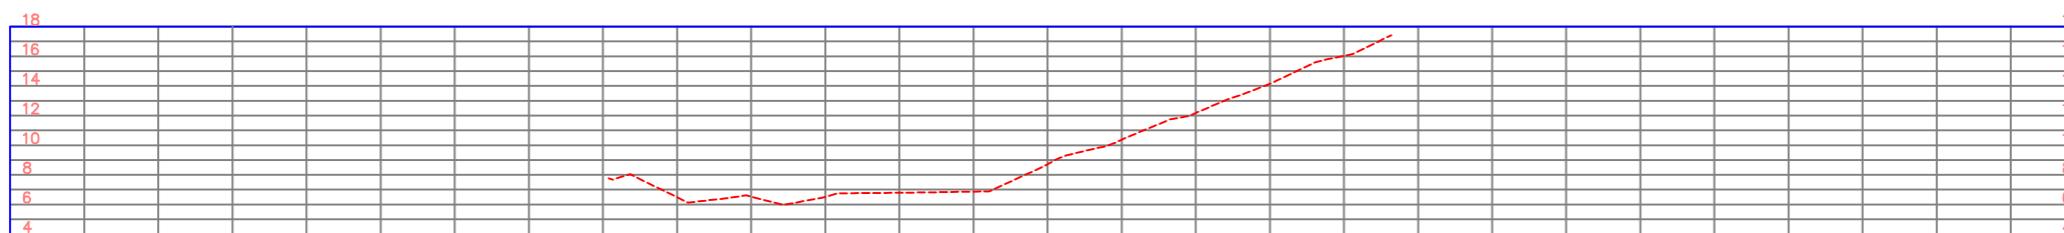

SECTION 1 - 1
SCALE 1 : 600

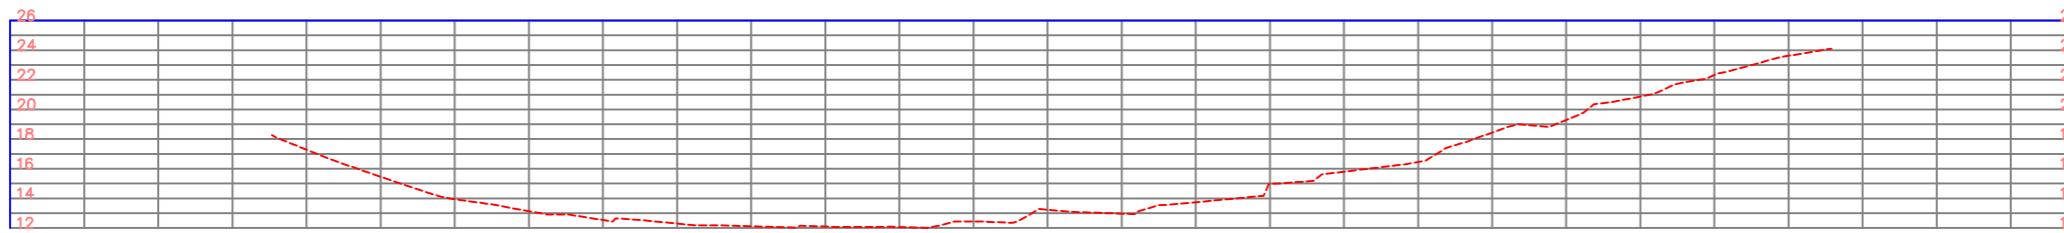

SECTION 2 - 2
SCALE 1 : 600

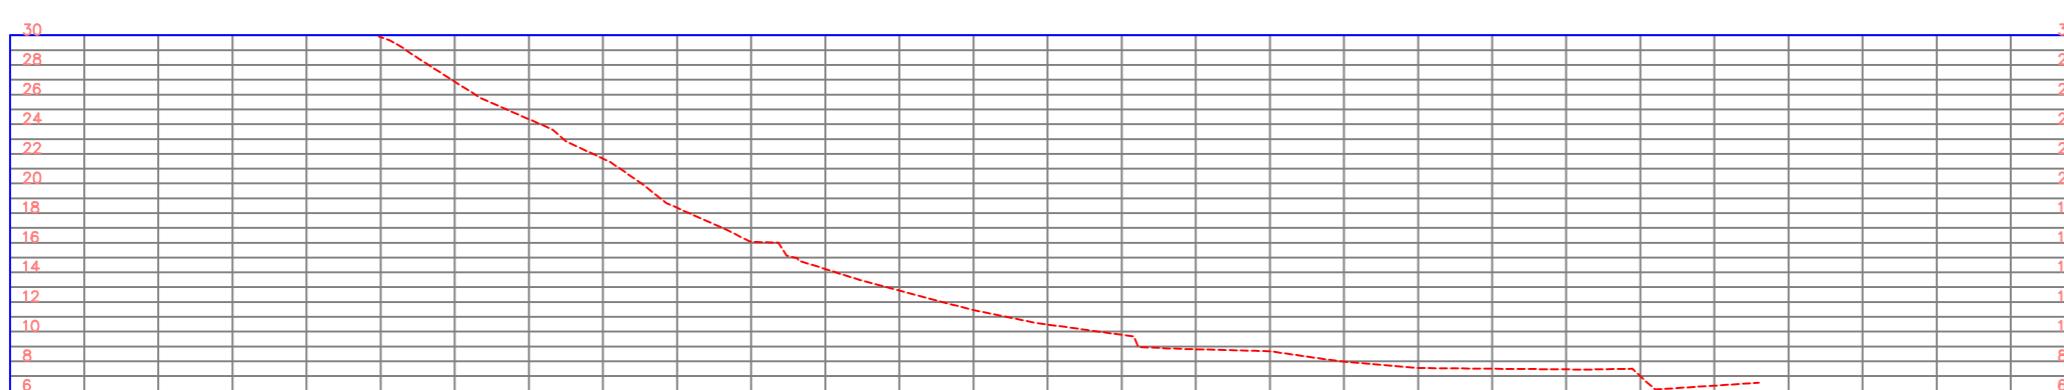

SECTION 3 - 3
SCALE 1 : 600



SECTION 4 - 4
SCALE 1 : 600

SUBMISSION	
FOR INFORMATION	
SURVEYED BY	CHECKED BY
NAUFAL MAJIST	EDI SUPRIYANTO,ST
DATE:	SCALE:
20MAY20	1 : 500
DWG. TITTLE :	
SECTION 1-1	SECTION 2-2
SECTION 3-3	SECTION 4-4

DWG. NO.

ESP/SRV/09/V/2020